Astraea as connected districts

A program and relationship study. Existing destinations anchor the plan; hotel buildings and new local connections remain proposals.

Homes and habitats

D04 aquatic / arboreal homes
D13-D17 residential neighborhoods
Known homes; grouping remains open

Grand botanical atrium

D02-D17 shared vertical landmark
Main terraces D06 / D09 / D12 / D16
Gardens, courts, reading and family edges

Distinct hotel buildings

Alternatives A and B on sheets 3-4
Local guest cores and service access
Exact rooms and tiers remain open

SHARED GUEST NETWORK

Active resort

D07 sport / movement
D08 pool / baths / wellness

Retail and local courts

D09 100 shops + 10 destinations
Markets, books, cafes, services

Dining and hospitality

D10 ten venues / 2,200 places
Food, social rooms, serving edges

Culture and outlooks

D11 theater / six cinemas
D12 library / salons / observation

Longitudinal promenades + five Townline catchments + existing express deck travel

Historical vertical relationships to retain in the study

Moonwell: D08 mineral springs + D09 Paper Moon books + D10 Lantern cafe. Vesper: 240-place restaurant, two levels and a waterfall connection to the aquatic district. Connections and exact geometry need reconciliation; see sheet 7.


SEPARATE SERVICE NETWORK

D01 logistics / laundry / supplies | D02 engineering | D03 crew homes | D05 care | D18 command

Evidence: atlas pp. 1-21; master chapters 4-7; latest user direction. Lines show relationships, not approved physical routes.

Longitudinal section and protected volume

Projected section with off-axis theater volume. Deck heights are exact; the local upper hull profile remains unresolved.

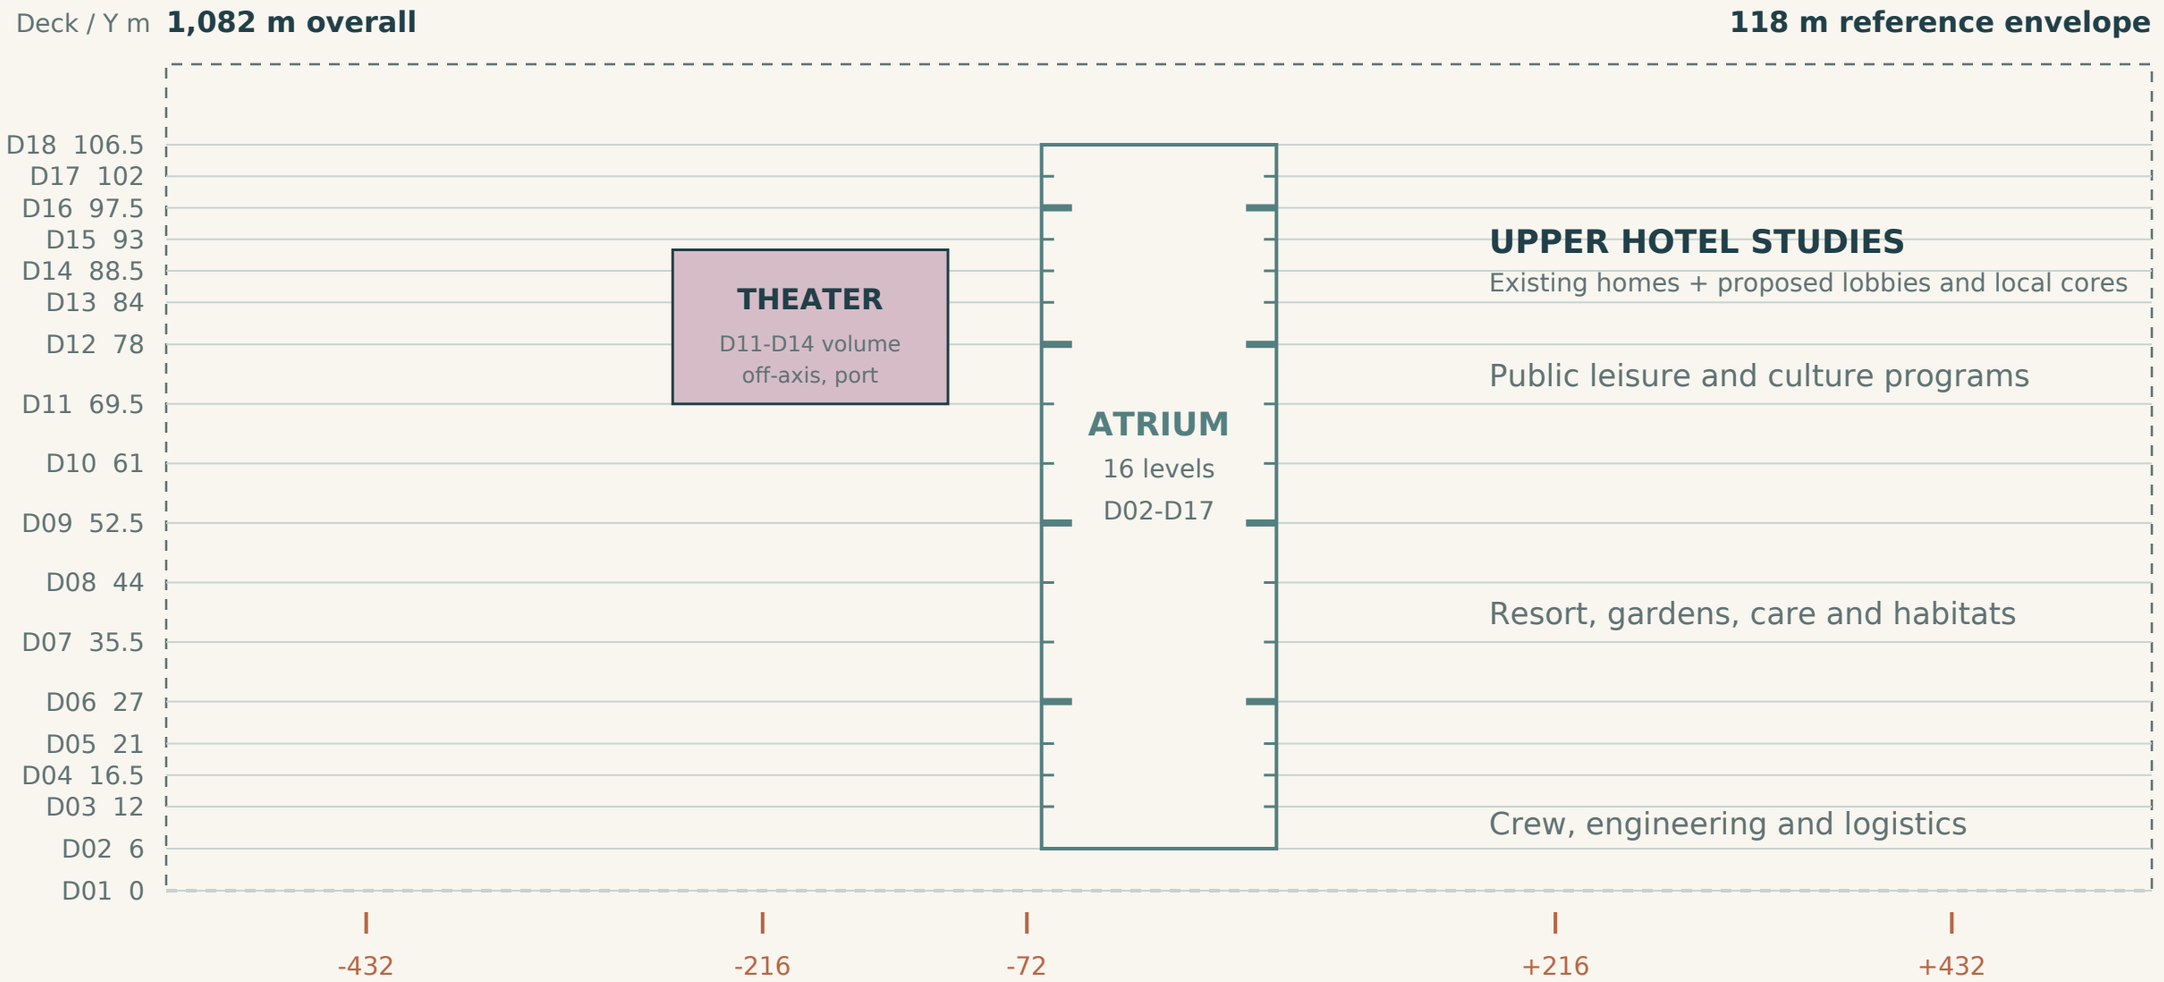

Townline stop Z coordinates (m). These are catchments, not hotel boundaries.


Atrium: Z -64..+64, X -48..+48. Theater: Z -265..-115, X -118..-34, top Y 91.5 m. Existing D12-D14 floor openings and D12/D13 gallery interfaces stay protected. Vertical exaggeration 3.82x; no new openings.

Still unresolved: upper hull clearance at every proposed building, local lift/stair shafts, multistory suite floor changes, court widths and the purpose of residual allocations. Every new vertical connection must be reconciled in plan and section.

Evidence: atlas pp. 2, 13-14, 21; source archive AUDITORIUMS.md and SHIP_DESIGN.md. Maximum envelope is not a roof design.


Alternative A Three distinct hotels with a deeper public base

A proposal for two different forward hotels and one quieter aft hotel. Strong individual identity; greater conflict-review burden on public decks.

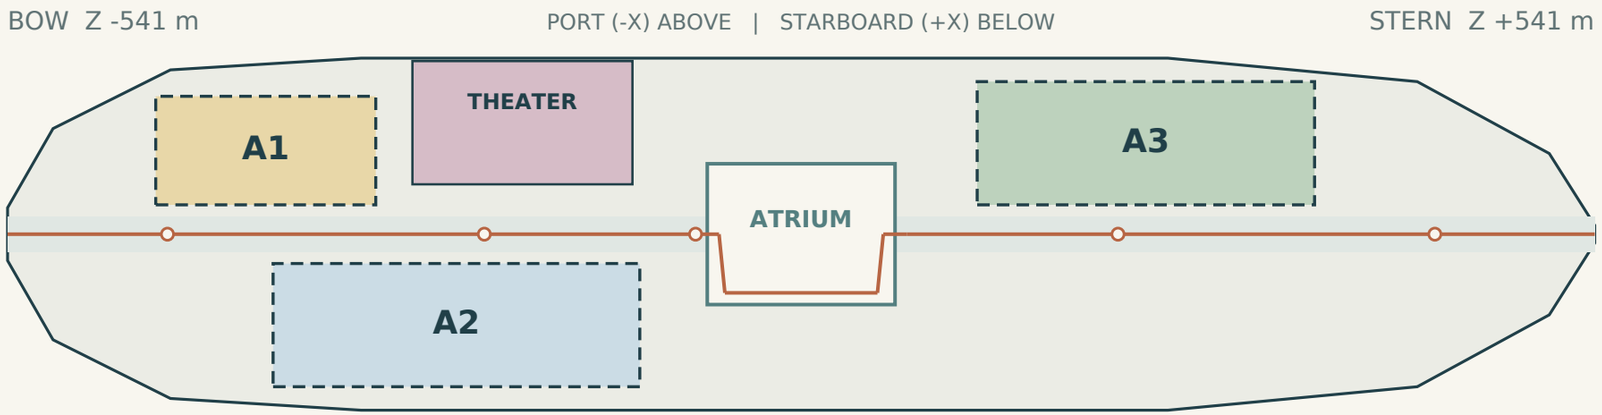

Plan-hull contour traced from the atlas. All colored hotel zones are NEW study allocations.

Tram bypass simplified; sculpted supporting floor ring omitted. No collision claim.

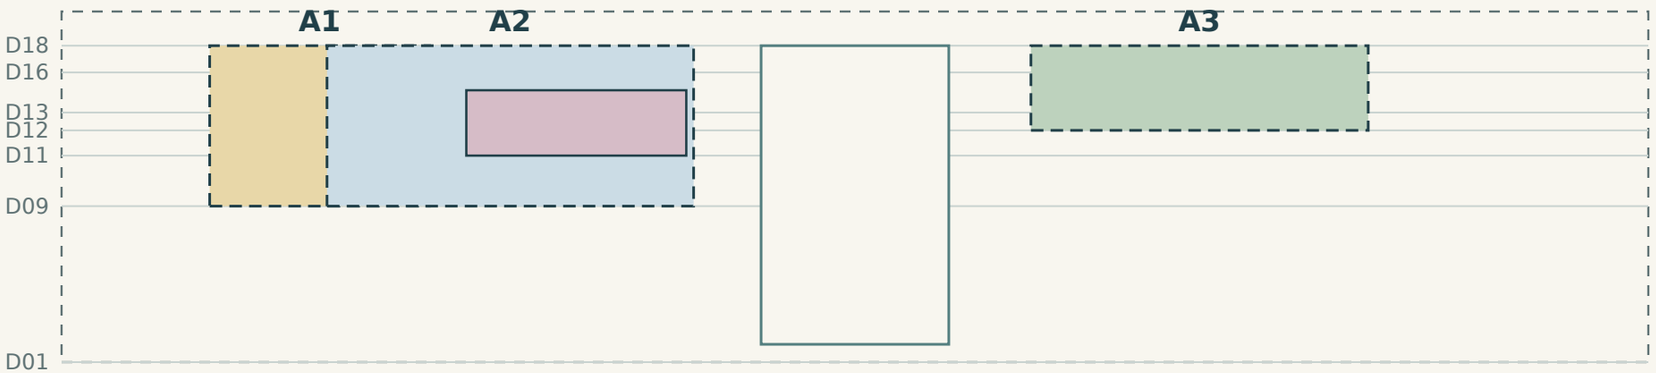

Projected section. Same-Z port/starboard hotels overlap here; they are separate masses in plan.

A1 Forward port hotel

Z -440 to -290 m
X -94 to -20 m | D09-D17

A2 Forward starboard hotel

Z -360 to -110 m
X 20 to 104 m | D09-D17

A3 Aft garden hotel

Z 120 to 350 m
X -104 to -20 m | D12-D17

No room counts assigned

The 1,000-unit ledger remains whole. These envelopes test relationships; they do not absorb or delete existing destinations.


Upper hull fit and local shafts are unresolved. No floor cuts, bridges or lift cabins are approved by these boxes.

Opportunity: Distinct scales and arrivals; hotel life can overlap retail, dining and culture without making one enormous undifferentiated accommodation bar.

Review before choosing: A1/A2 study volumes include existing D09-D12 programs. Cinemas, shops, dining and observation remain protected allocations until exact IDs and alternatives are reviewed.


Alternative B Four smaller hotels with paired courts to resolve

Paired forward and aft hotels above the public decks. Local court locations are unresolved and are not drawn.

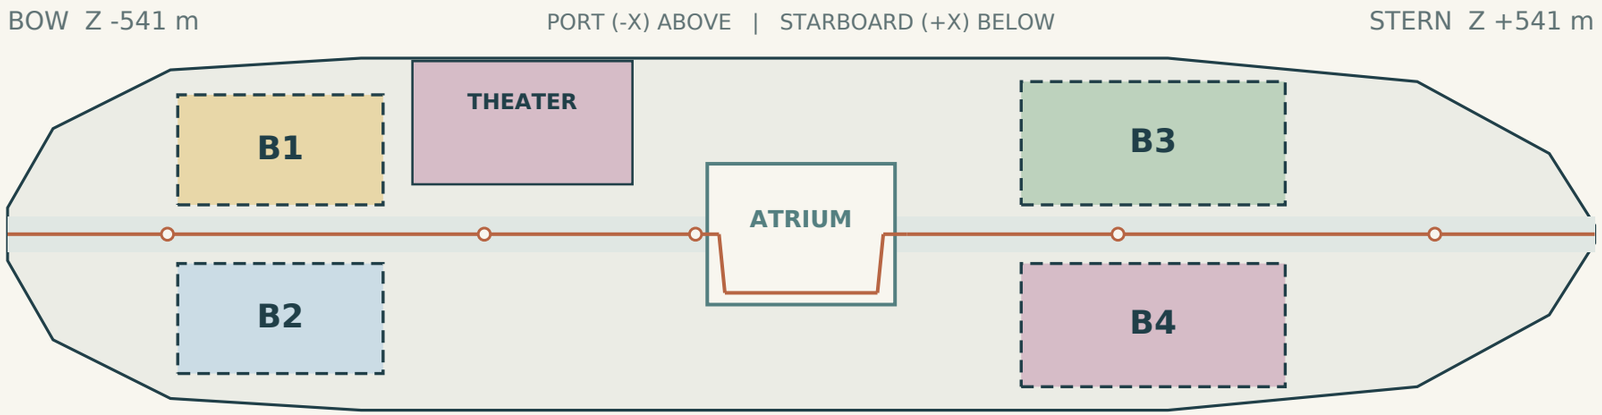

Plan-hull contour traced from the atlas. All colored hotel zones are NEW study allocations.

Tram bypass simplified; sculpted supporting floor ring omitted. No collision claim.

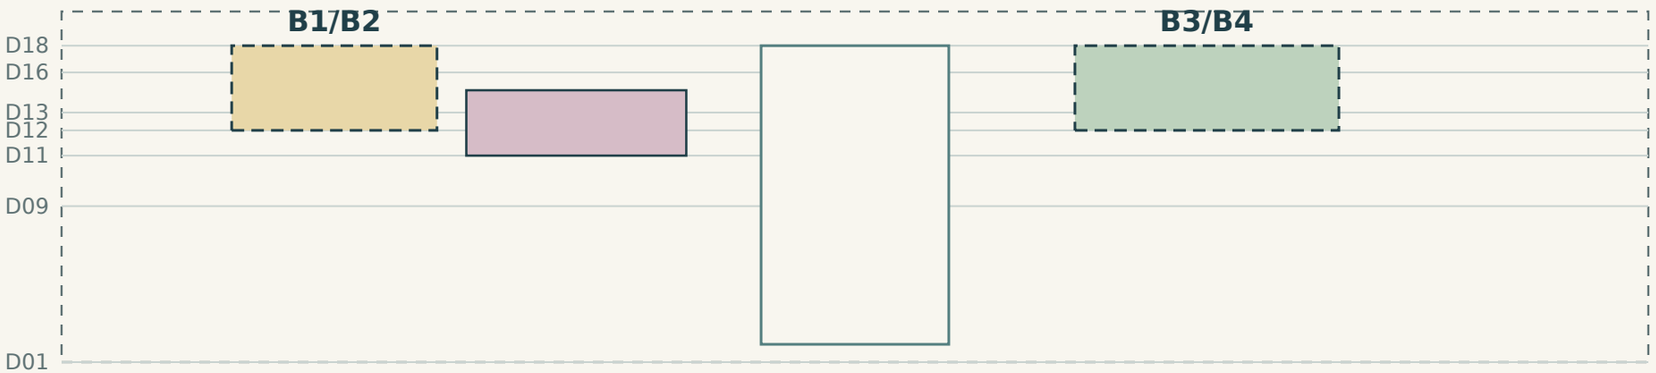

Projected section. Same-Z port/starboard hotels overlap here; they are separate masses in plan.

B1 Forward port hotel

Z -425 to -285 m
X -95 to -20 m | D12-D17

B2 Forward starboard hotel

Z -425 to -285 m
X 20 to 95 m | D12-D17

B3 Aft port hotel

Z 150 to 330 m
X -104 to -20 m | D12-D17

B4 Aft starboard hotel

Z 150 to 330 m
X 20 to 104 m | D12-D17

No room counts assigned

The 1,000-unit ledger remains whole. These envelopes test relationships; they do not absorb or delete existing destinations.

Upper hull fit and local shafts are unresolved. No floor cuts, bridges or lift cabins are approved by these boxes.

Opportunity: Clearer compact neighborhoods and potential quieter upper courts. Public dining, retail and resort remain a shared layer below, reached by local cores that still need a real footprint.

Review before choosing: Additional lift/stair/service cores consume area. D12 existing library/observation uses and D13-D17 room allocations still need a complete reconciliation.

Base: atlas p. 13 hull and protected geometry. Hotel coordinates/heights are explicit proposals. Not a final 1,000-room allocation.

Allocation and constraint ledger

One authoritative program, with dated evidence separated from new proposals. All 1,462 surviving IDs are preserved in the editable crosswalk.


Item	Established or retained baseline	Open decision / action
Hull and decks	18 decks; 1,082 m length; 240 m max beam; 118 m envelope	Use exact floor elevations; verify local roof/side clearance
Guest accommodation	1,000 units; 81 luxury included, not additional	50 deluxe / 25 premium / 5 royalty / 1 supreme; exact rooms open
Population	2,000 hard passenger cap; normal 1,200-2,000	Do not revive historic 2,500 maximum or force full occupancy
Crew homes	400 crew including player; player shares a staff room	Old private-player-cabin allocation needs explicit reconciliation
Atrium	96 x 128 m opening D02-D17; principal terraces 06/09/12/16	Purposeful courts and edges; preserve open volume and interfaces
Theater	2,200 places; 84 x 150 x 22 m; D12-D14 floor openings	Protect D12/D13 gallery interfaces, access and residential detours
Retail and dining	100 shops + 10 larger D09 places; D10 has 2,200 meal places	Reconcile actual footprints before any hotel overlap
Transport	Five Townline catchments; express interface; tram bypass	Local hotel cores need footprints; panoramic lifts not verified
Hotel alternatives	A: three study hotels; B: four smaller study hotels	No chosen scheme, assigned IDs, capacity or approved new holes
Luxury sections	Multistory upper-level rooms are current direction	Exact floor relationships, suite sizes and privacy need review
Moonwell / Vesper	Historical district links and Vesper 240-place program retained	Names, multi-level boundaries and water connection unresolved
Asset planning	Catalogue components can be tailored while planning evolves	Keep mating interfaces adjustable; no claimed game adoption

Crosswalk discipline: existing_id and historical program remain unchanged; proposed_hotel_id is null for every record. New hotel membership needs explicit reconciliation. Older room-class and crew-home assumptions are retained as history, not silently adopted as latest canon.

Evidence: latest user canon; atlas; master source archive coverage ledger. Historical source checks do not verify a recovered runtime.

A district-specific kit with a real interface

First paired target: D09 salon and starboard atrium arrival. Historical interfaces guide new adjustable components.

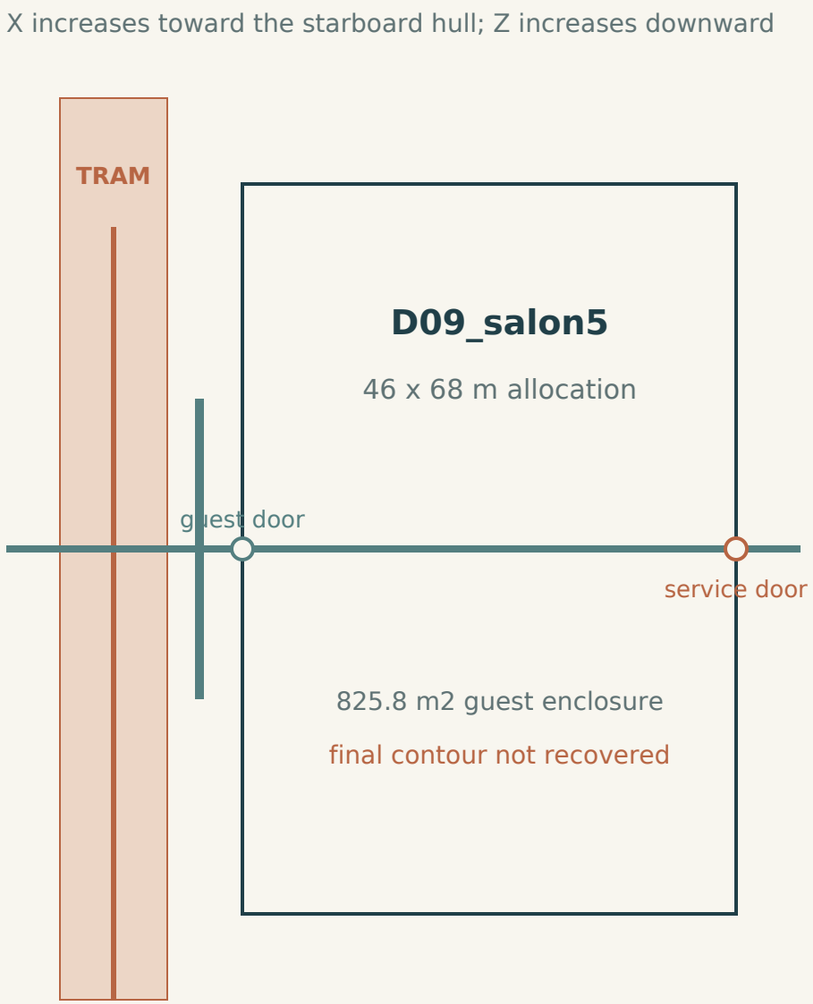

28 m connected terrace at Z -14..+14
X35..45 tram reserve and the Z0 arrival/service axis stay clear.

Six tailored junctions and built-ins

01 Deep public portal return
Meet the existing X52 entry and preserve its turning landing.

02 Coved wall-to-ceiling transition
Rib, light channel and soffit share a real joined profile.

03 Quiet book-and-acoustic return
Integrate shelf depth, sheltered seating edge and local light.

04 Planted court-to-seat junction
Connect garden edge and usable resting place without a new room.

05 Terrace rail-to-portal terminal
Resolve the actual garden-facing threshold and guard seam.

06 Protected service/storage return
Frame the X98 service access with useful, shallow support depth.

Height evidence: D09 floor +52.5 m; D10 +61 m; archived usable budget 8.25 m. Later component brief limits a quiet booth to 7.2 x 5.4 x 3.8 m and a tea bay to 6 x 3 x 3.2 m. These are historical authoring limits, not proof of recovered fit.

Sources: D09_CONNECTED_SALON.md; D09_COMPOSITION_CONTRACT.md. Warm ivory / blue-green recess / warm wood / restrained brass.

Moonwell and Vesper remain in the district plan

Preserve the pre-loss design relationships without inventing their missing shafts, room boundaries, floor openings or water geometry.

Moonwell three-level neighborhood

D10 +61 m

Lantern cafe in conversation
Historical ID candidate: D10_banquet2
Archive name: Lantern restaurant / 240 places

D09 +52.5 m

Paper Moon bookshop
D09_books2 / Paper moon books
Quiet browsing and shared social threshold

D08 +44 m

Mineral baths / springs
D08_bath2 / Mineral springs
Wet/dry threshold and towel/service approach

These are a historical conversation grouping plus surviving ID candidates. A physical shared court, local lift, stair or open void has not been recovered. Exact room-name equivalence needs review.

Vesper dining and aquatic connection

Vesper restaurant / 240 places

D10_banquet7 is the surviving Vesper dining record. The conversation reports two levels and a connected waterfall. The second level and waterfall route are not established by the archived allocation.

Historical connection

Aquatic district

A real adjacency goal to preserve. Do not equate the visual waterfall with a proven fluid system, floor opening or navigable route.

What this should drive in the next kit

A coordinated wet-to-dry threshold family; quiet bookshop edge; cafe service front; stacked wayfinding; rail/soffit transitions; and a water-facing dining edge. First establish the interface dimensions and actual neighboring rooms, then author the connected components together.


Do not count a new cafe or another 240 seats from a naming difference.

Sources: surviving IDs in whole_ship_coverage.json; historical conversation reports. Dashed links are unverified connections.

One connected assembly to test first


An adjustable proposal joining arrival, reading bay and planted return. All positions need recovered-boundary review.

Plan connected threshold and bay

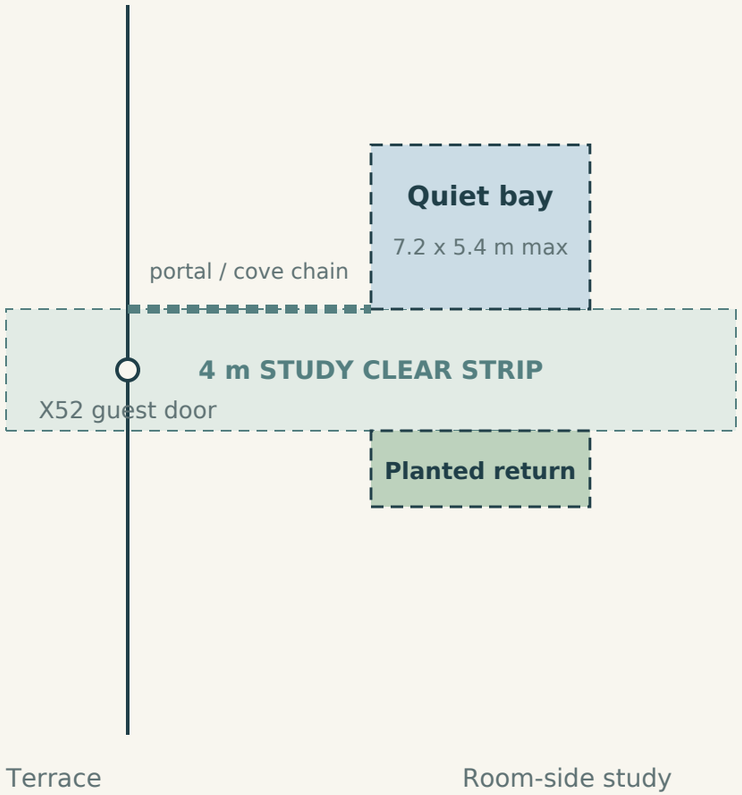

New study coordinates: quiet bay X60..67.2 / Z-7.4..-2; planted return X60..67.2 / Z+2..+4.5. The final 825.8 m2 room contour is missing, so these are candidate positions only.

Section low bay and clear route

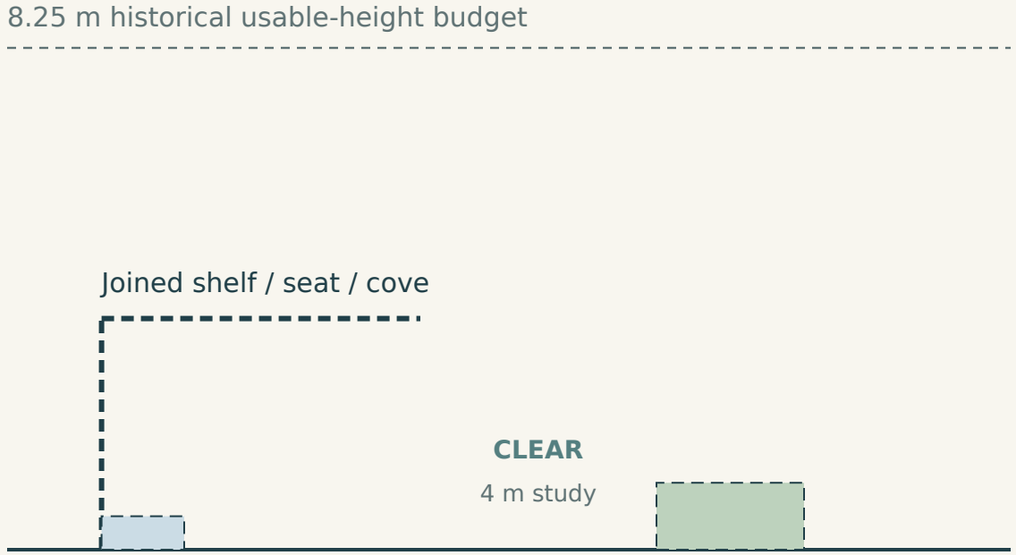

D09 +52.5 m | Z cross-section at proposed X64

The low bay uses the later 3.8 m maximum booth brief. Its ceiling must terminate into the enclosing return, with a joined light channel. The wider room ceiling remains unresolved.

Preserve the actual door aperture, turn landings, Z0 route, X35..45 tram reserve and both service/public doors. The 4 m strip is a proposed QA allowance, not a proven body/cart clearance result.